

樓梯(一般綁法)

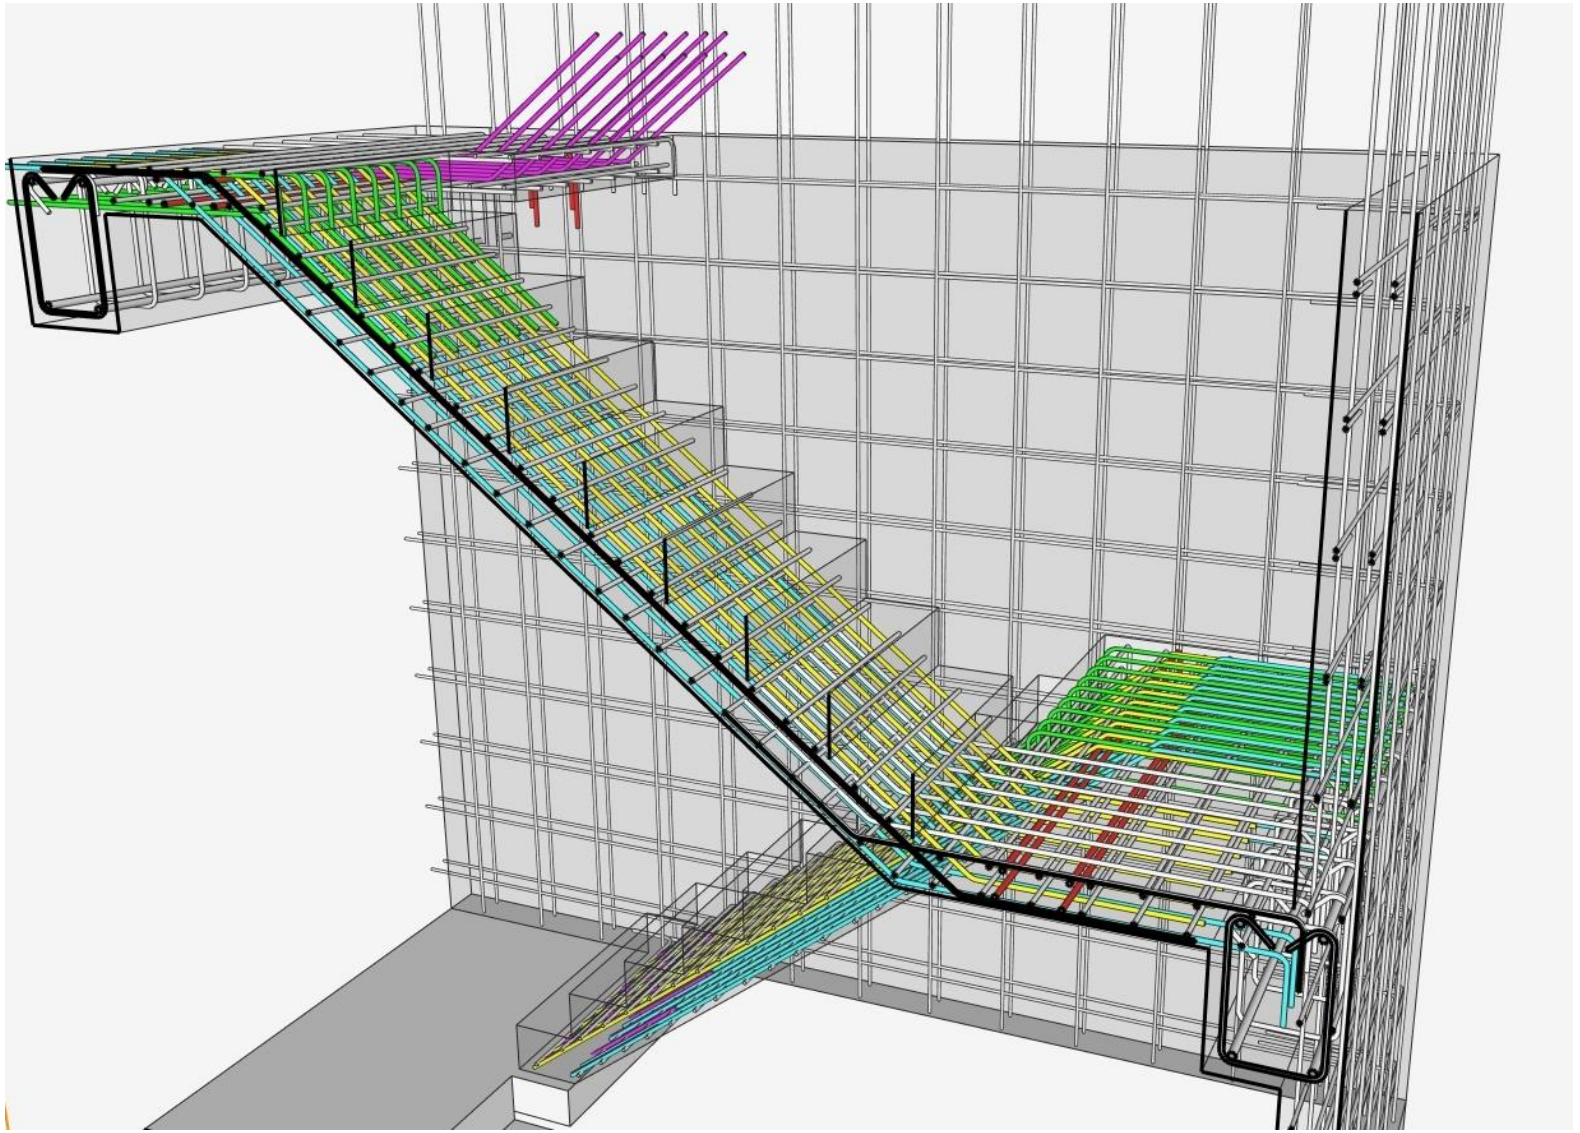

樓梯(一般綁法)

樓梯鋼筋

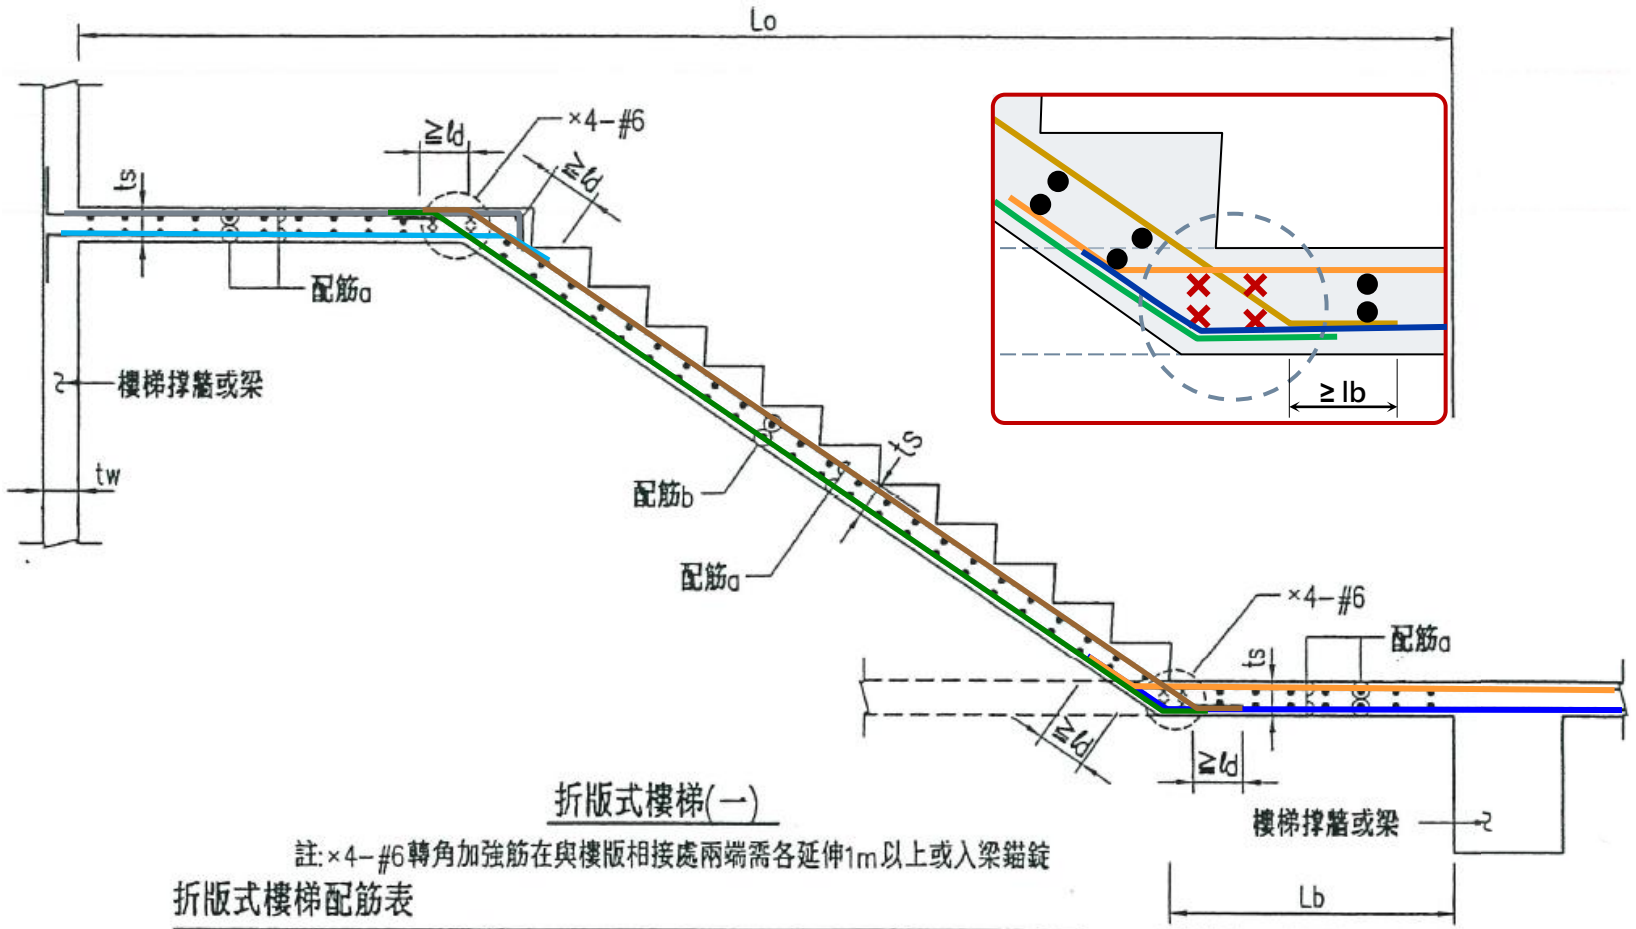

折版式樓梯(一)

註:×4-#6轉角加強筋在與樓版相接處兩端需各延伸1m以上或入梁錨錠

折版式樓梯配筋表

跨距 Lo	樓梯版			樓梯撐牆厚
	最小版厚 ts(cm)	配筋 a	配筋 b	tw(cm)
Lo≦4.0m	15	#4@12	#3@18	≧15

樓梯若與另有編號配筋之樓版相接(如虛線所示),×4-#6仍需配置,且若離梁(Lb)在1.5m以內時,則樓梯線筋(配筋a)需延伸至入梁ld。

樓梯(一般綁法)

樓梯

筋

施

作

參

考

