


# RC牆鋼筋施工程序與檢查點

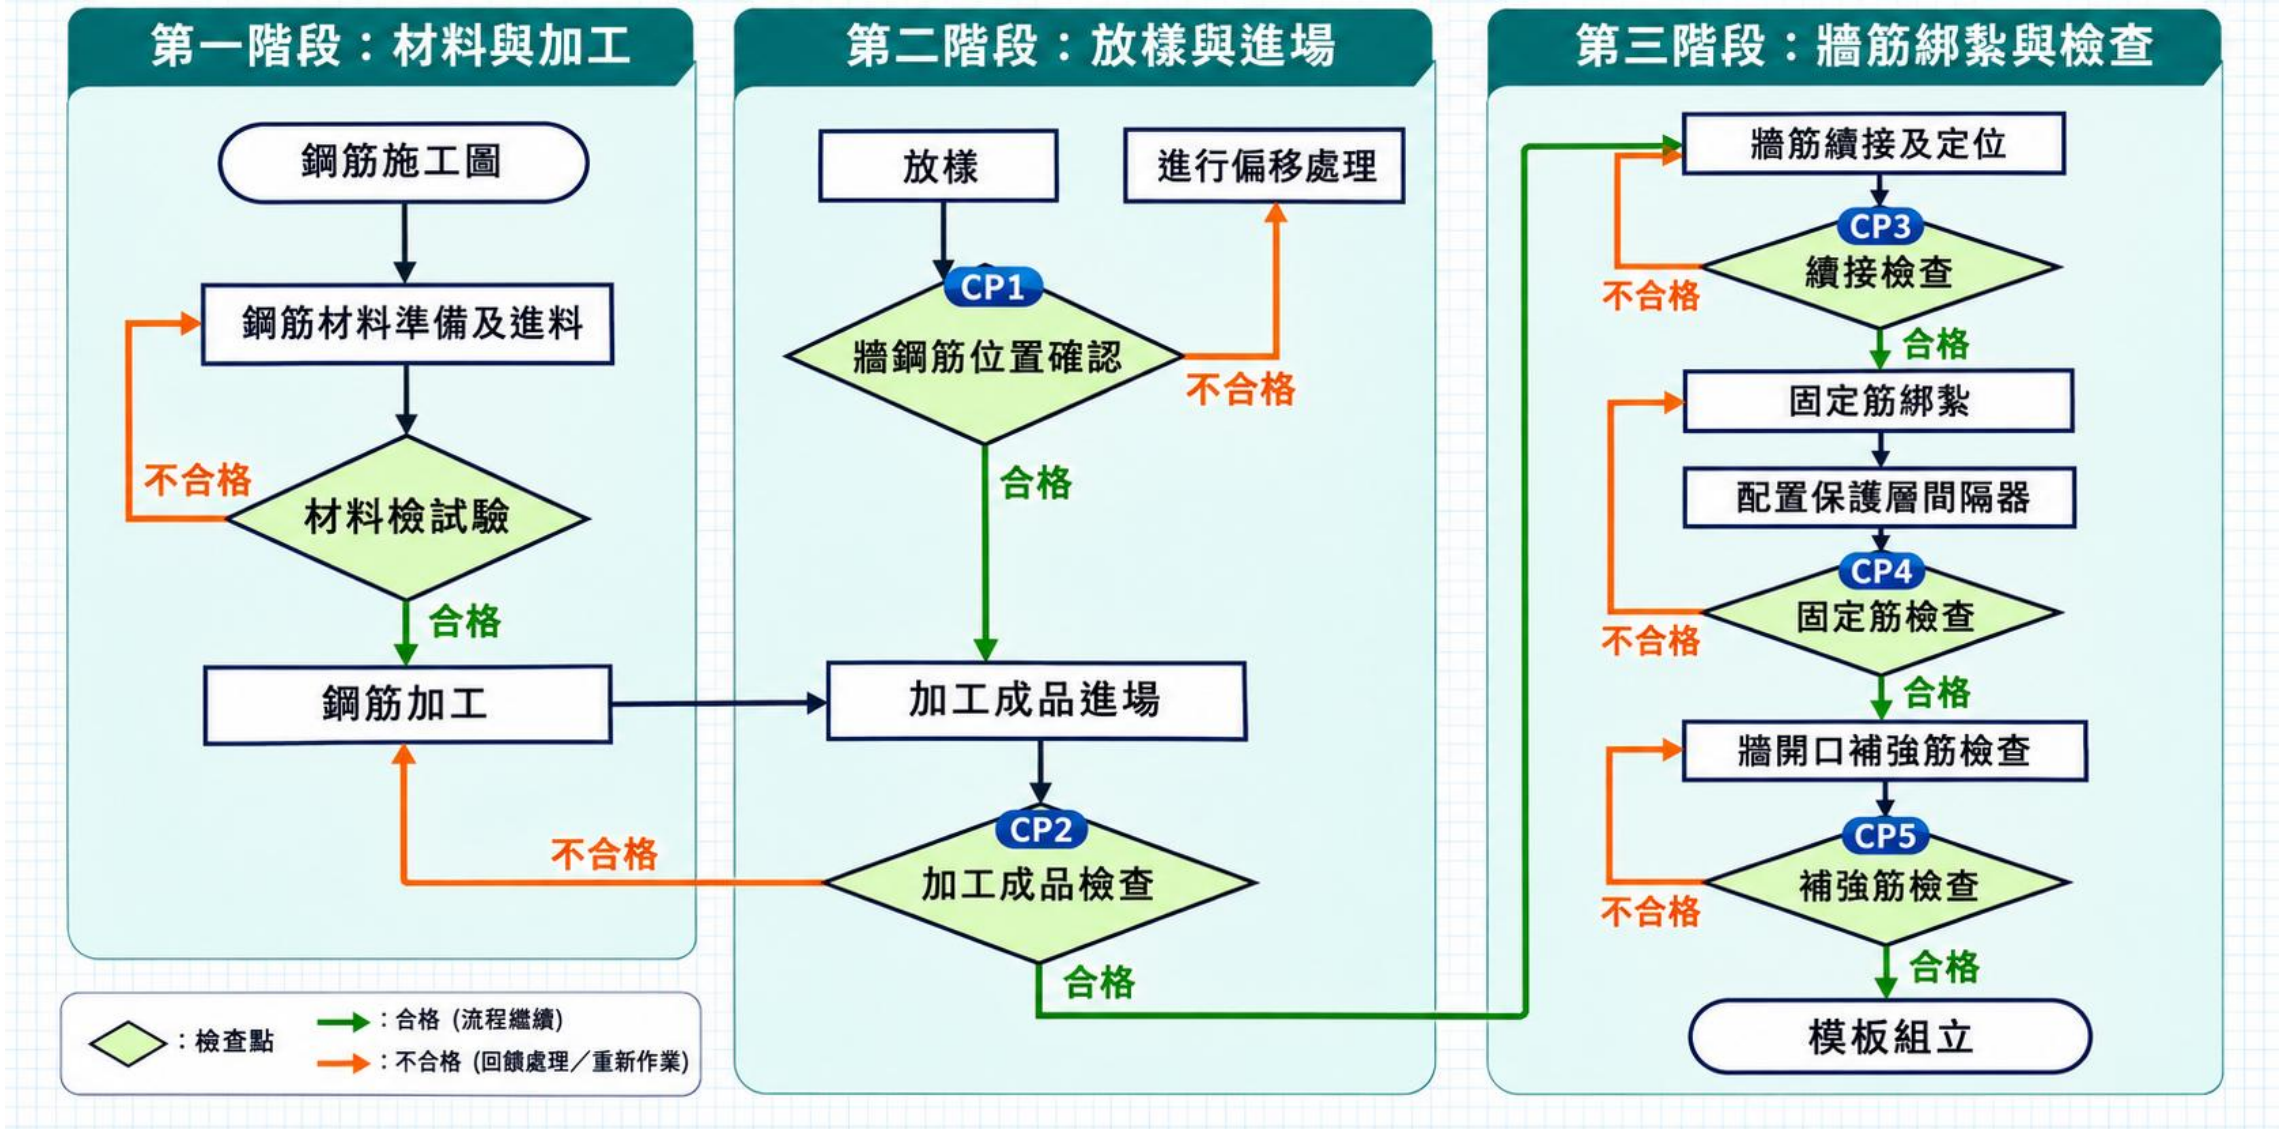




# 牆配筋標準圖

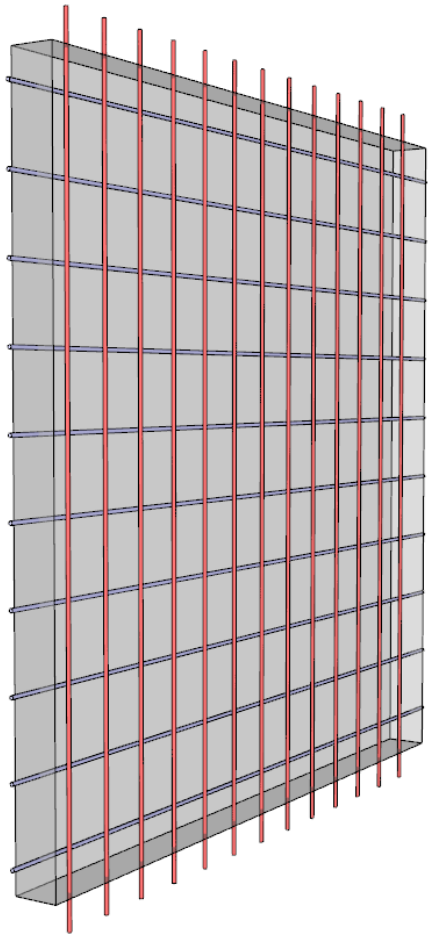


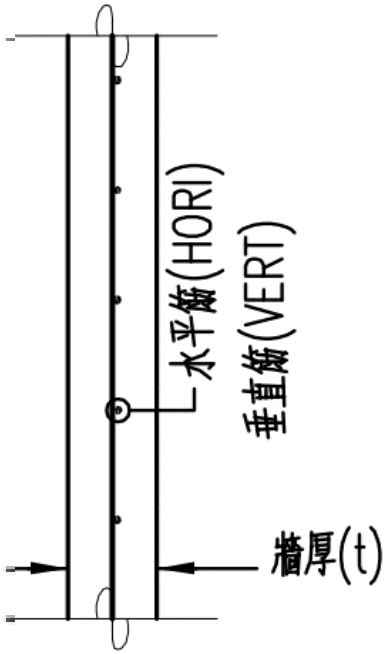



單排配筋(剖面)

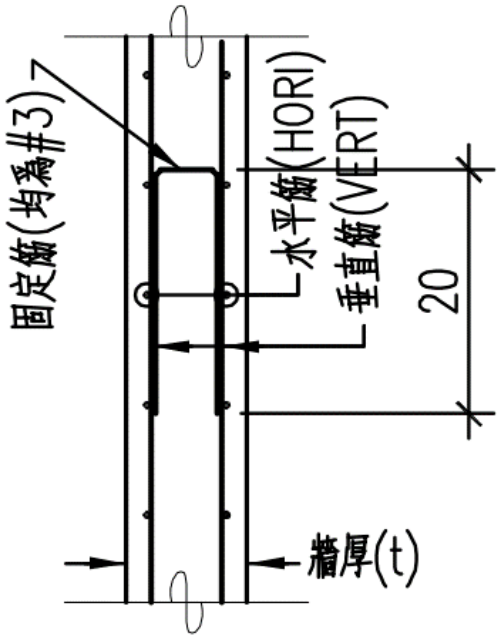



雙排配筋(剖面)

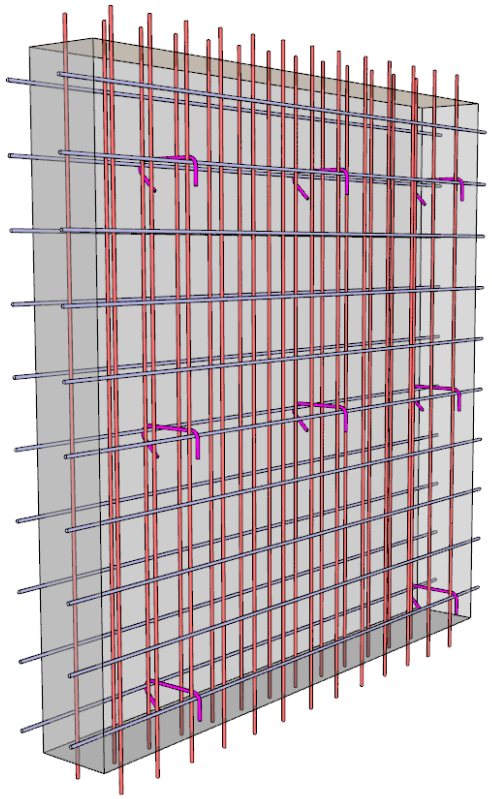

# 牆固定筋間距

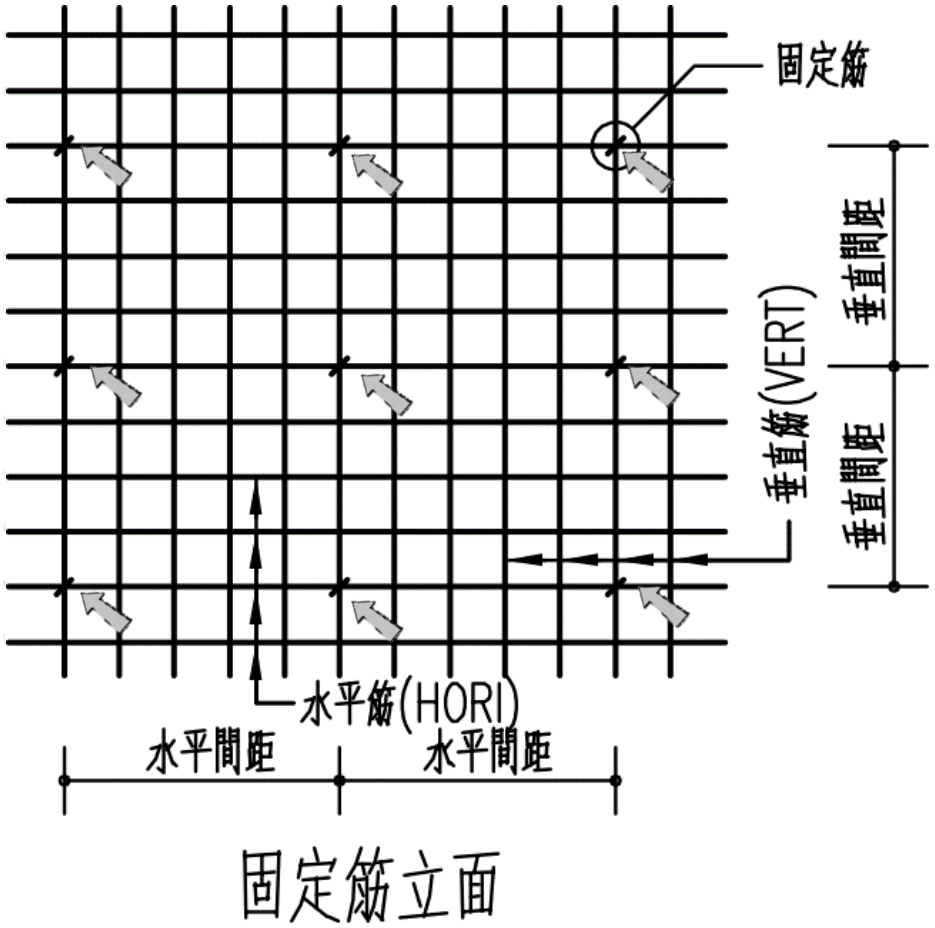



固定筋立面

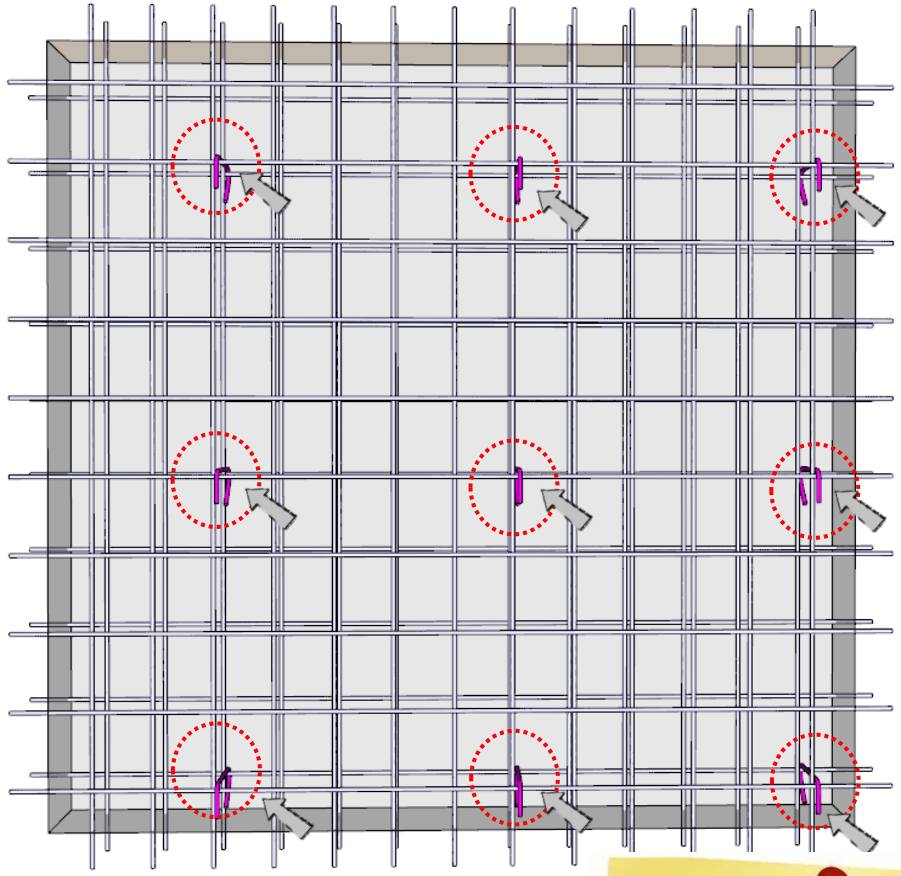


Tips:
牆固定筋的配置原則一般採用:水平間距為垂直筋間距之5倍，垂直間距為水平筋間距4倍。

# 牆角隅補強

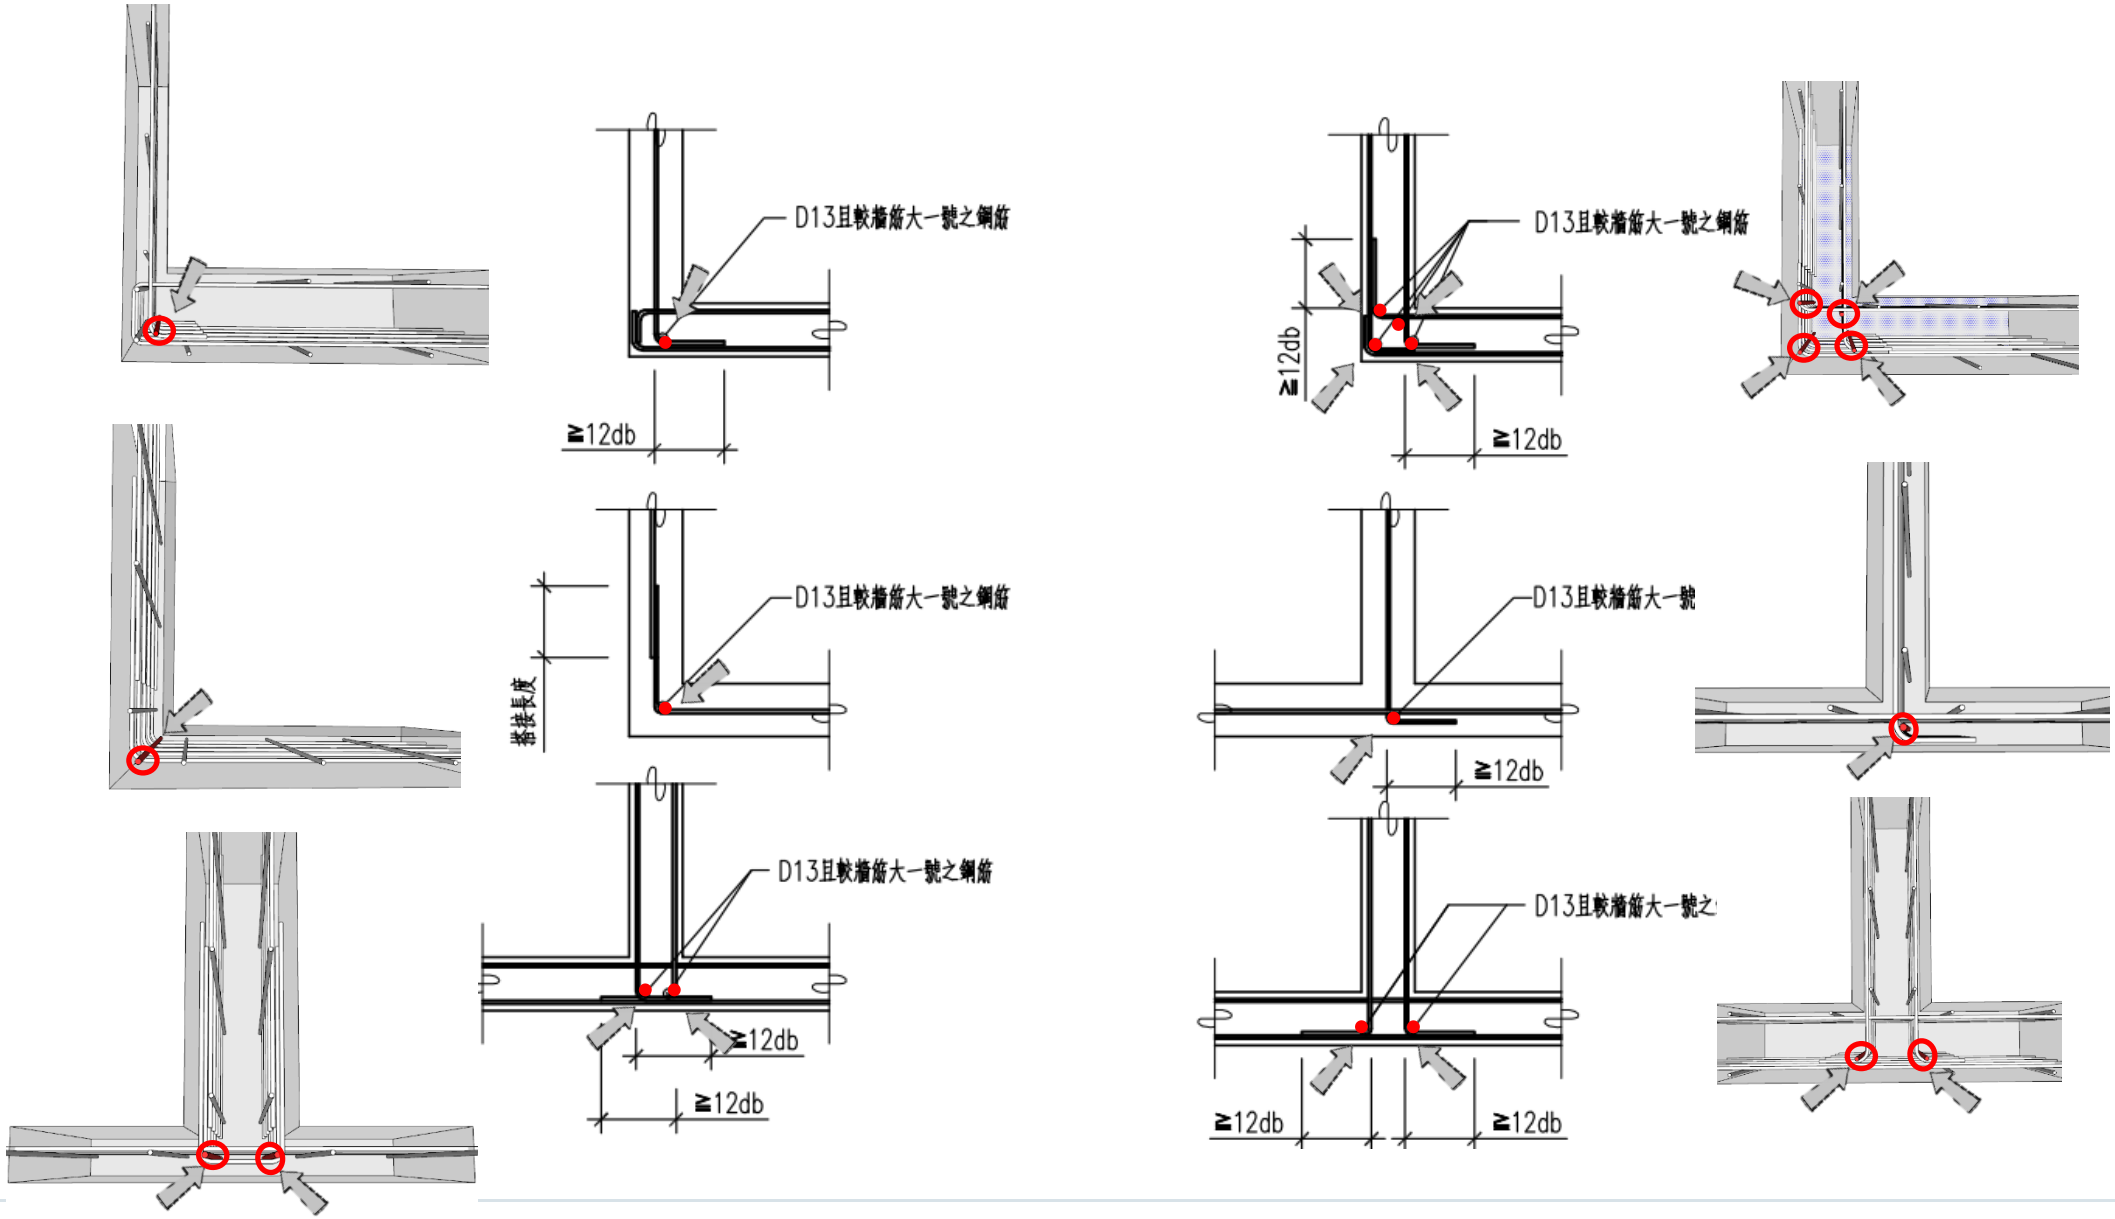


D13且較牆筋大一號之鋼筋
≧12db
搭接長度
D13且較牆筋大一號
≧12db
D13且較牆筋大一號之鋼筋
≧12db
≧12db
D13且較牆筋大一號之鋼筋
≧12db
D13且較牆筋大一號
≧12db
D13且較牆筋大一號之
≧12db
≧12db


# 牆開口補強

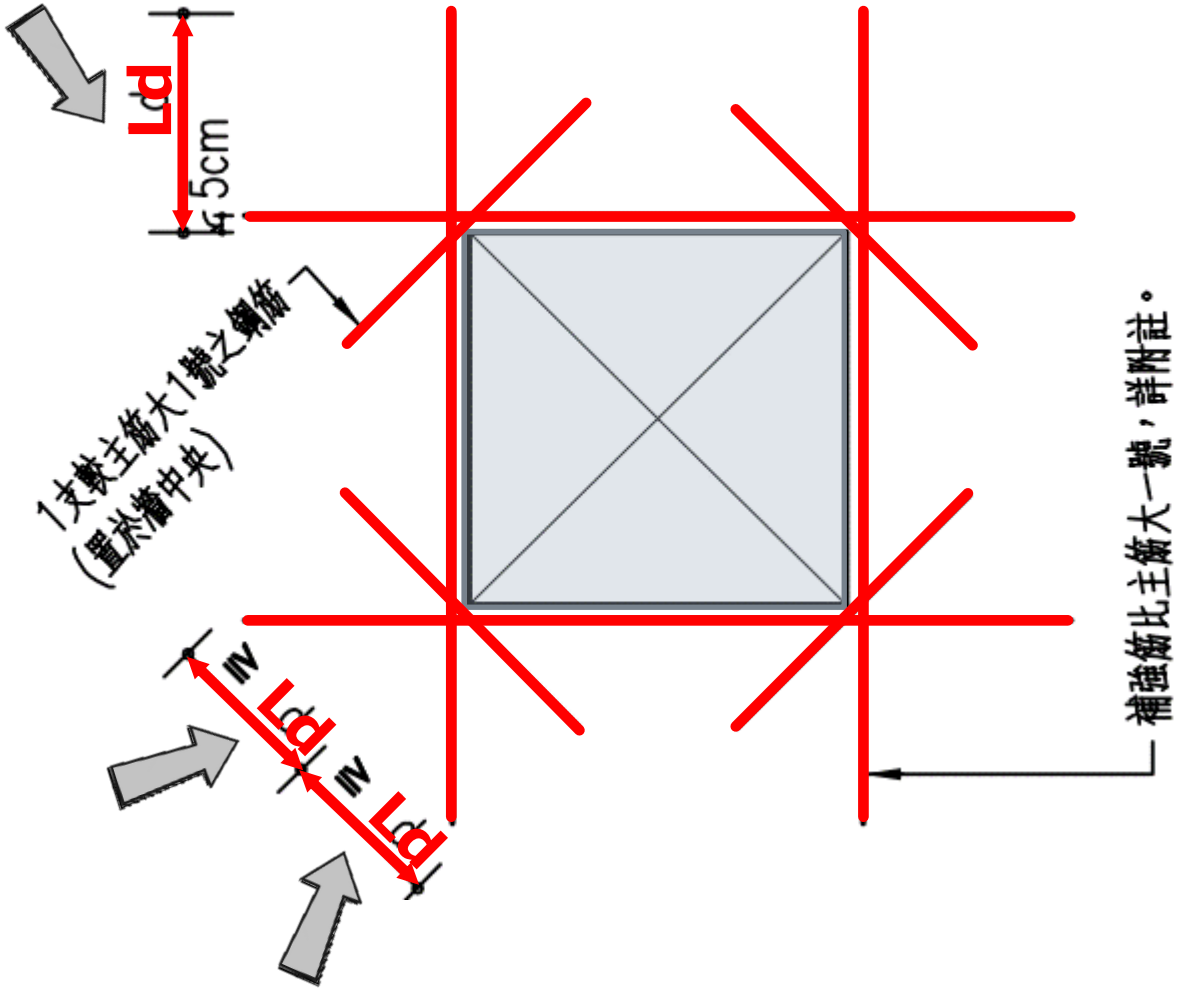


附註：牆主筋為單排時，補強筋亦為單排置於牆中央，
，牆主筋為雙排時，補強筋亦為雙排，如圖所示。

# 牆開口補強



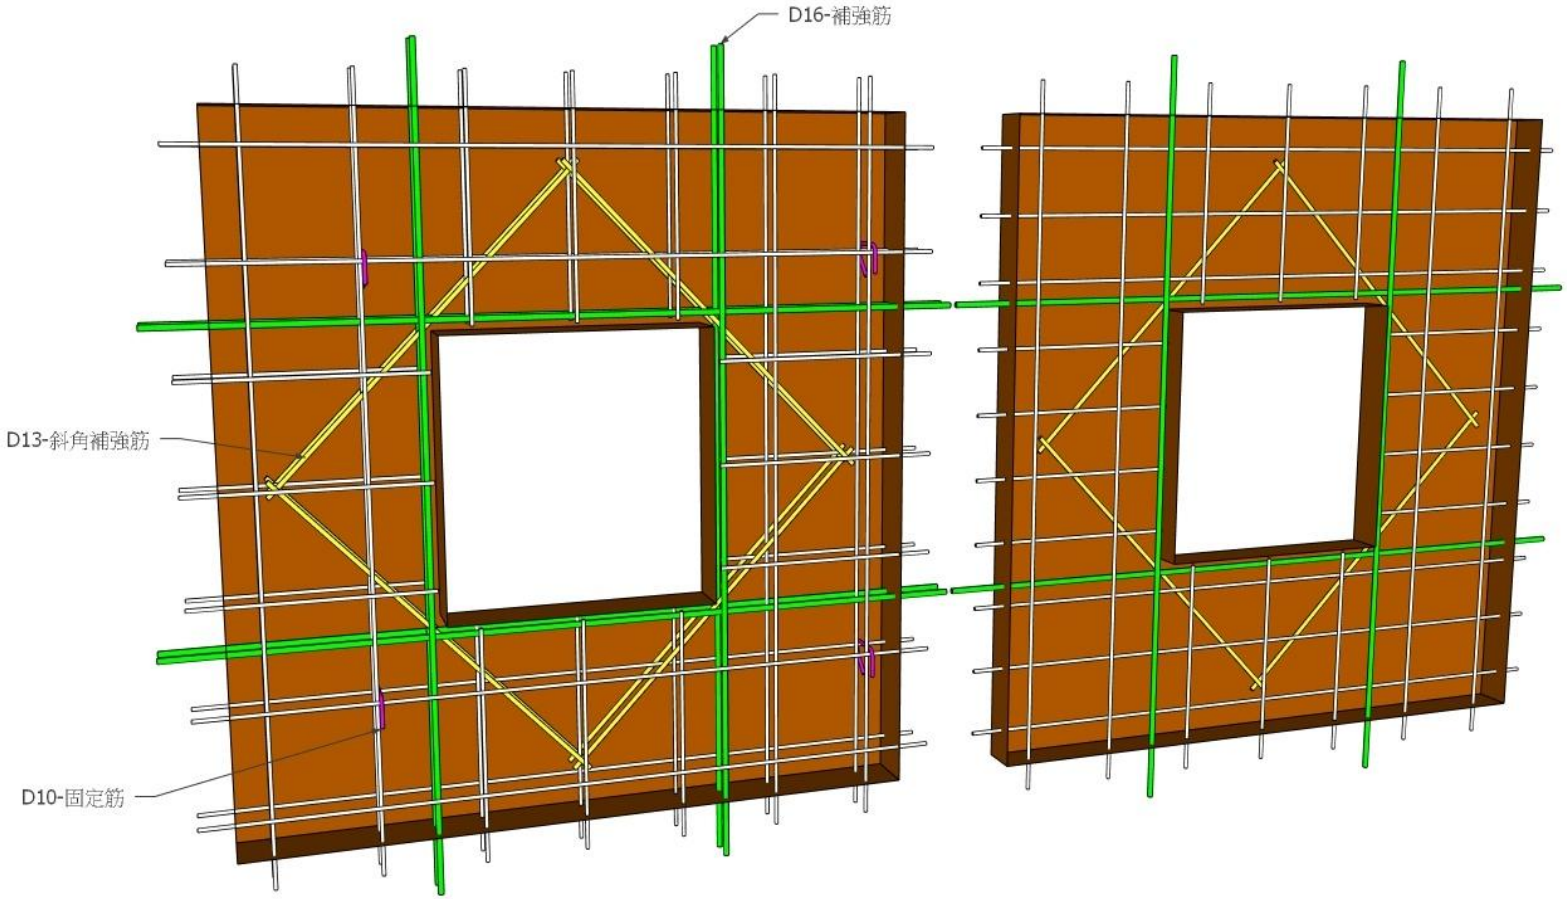


：牆主筋為單排時，補強筋亦為單排置於牆中央，
，牆主筋為雙排時，補強筋亦為雙排，如圖所示。